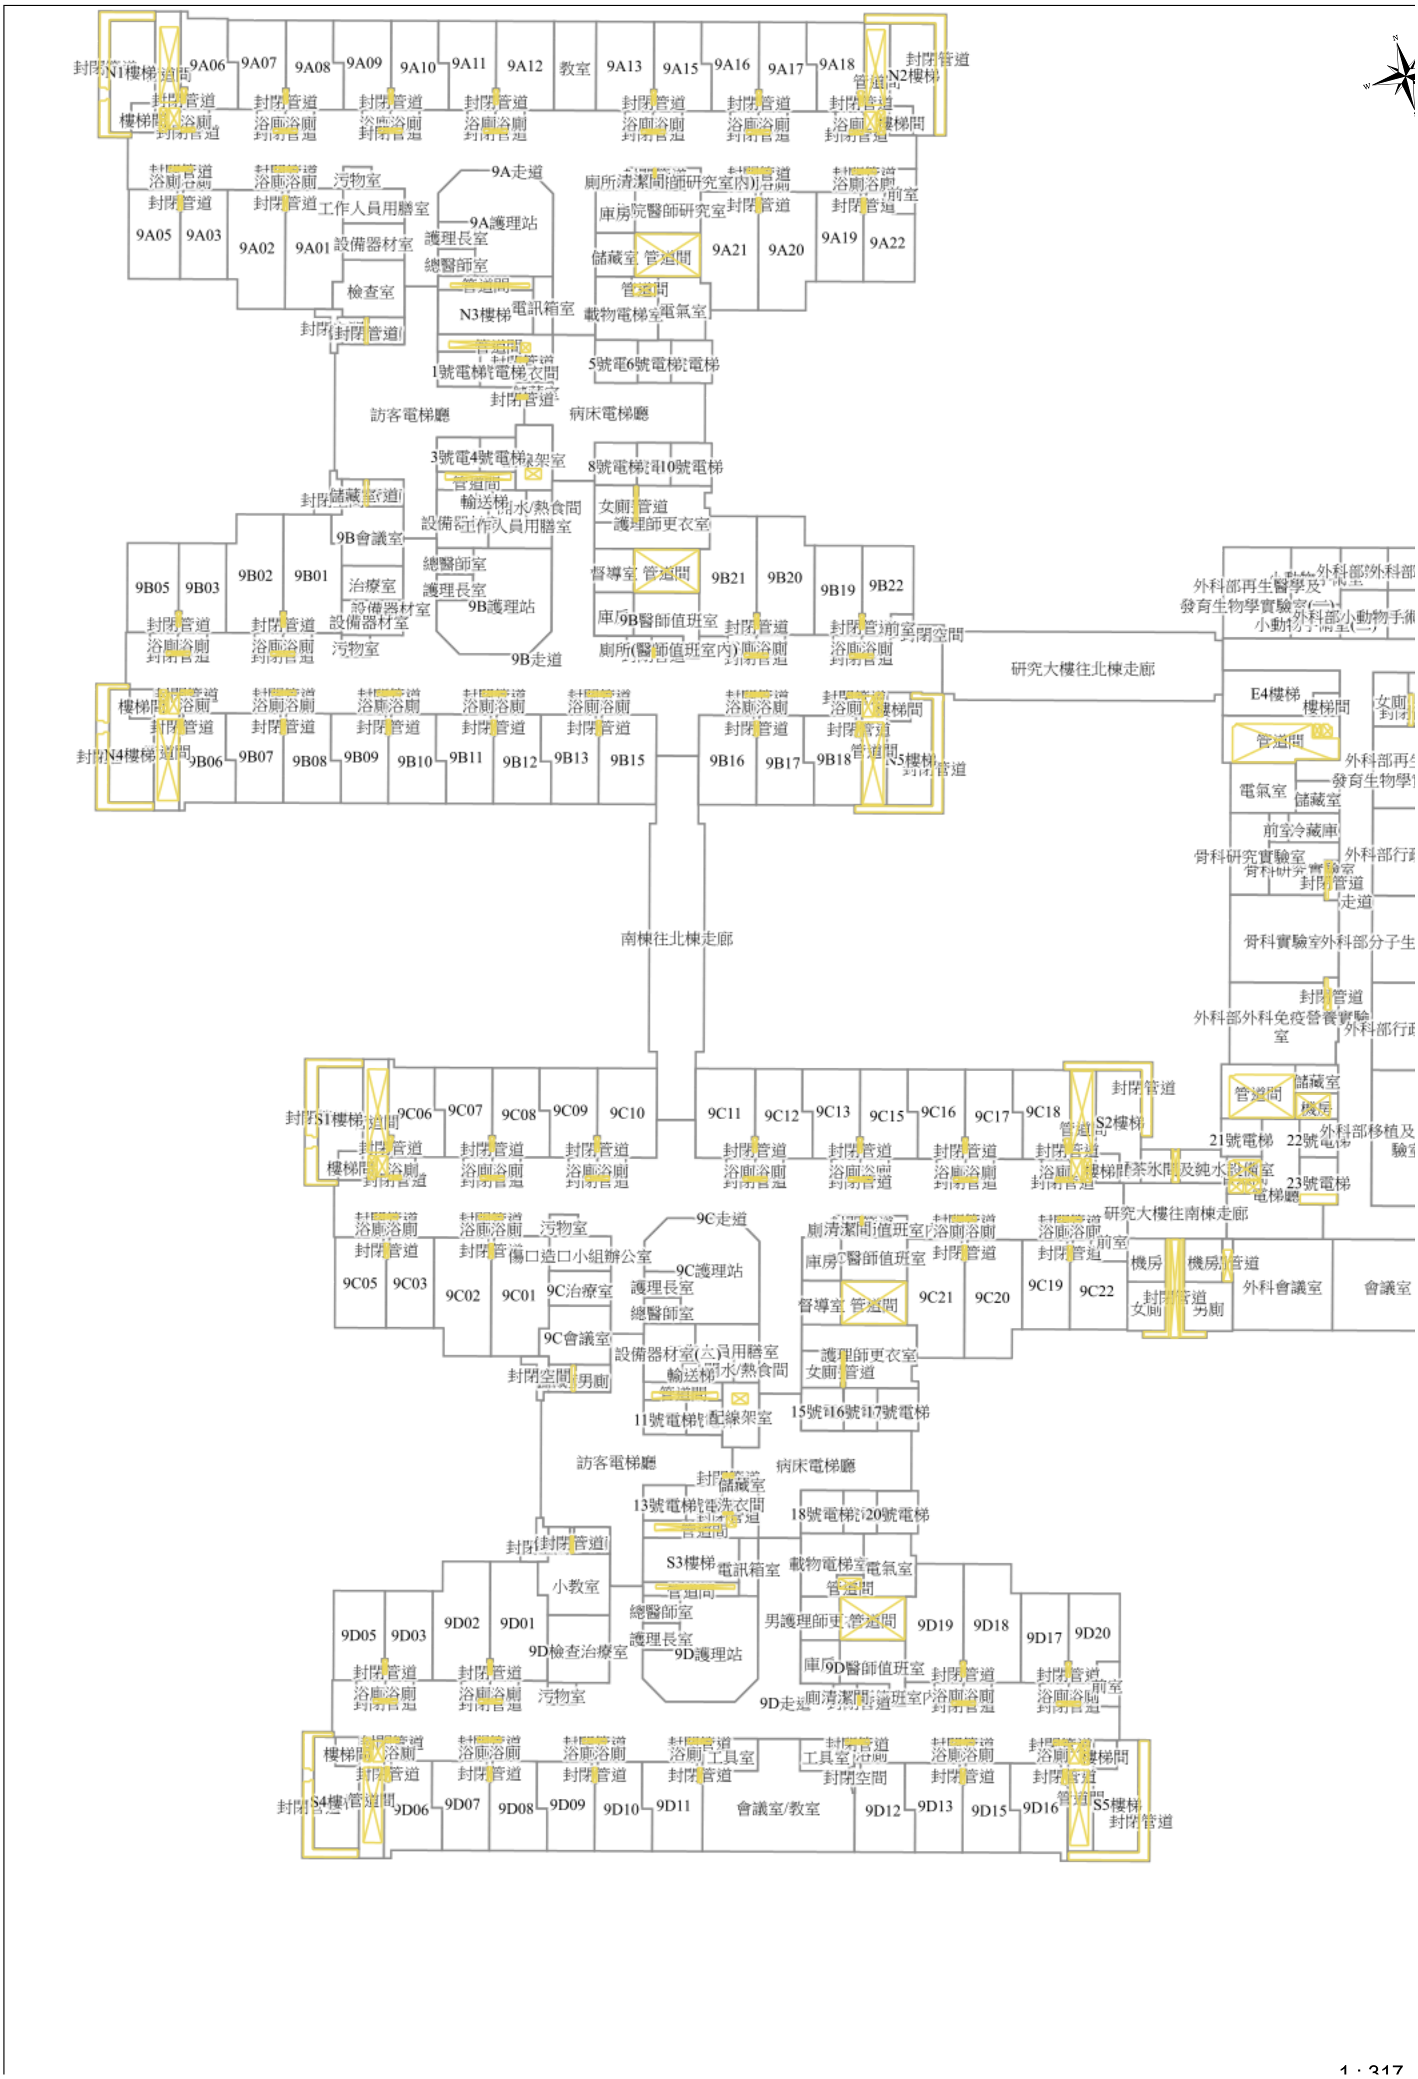
封閉管道
N1樓梯
管道間
9A06
9A07
9A08
9A09
9A10
9A11
9A12
教室
9A13
9A15
9A16
9A17
9A18
N2樓梯
樓梯間
浴廁
浴廁浴廁
封閉管道
污物室
9A走道
工作人員用膳室
9A護理站
護理長室
設備器材室
總醫師室
9A05
9A03
9A02
9A01
檢查室
N3樓梯
電訊箱室
廁所清潔間
醫師研究室
庫房
院醫師研究室
儲藏室
管道間
載物電梯室
電氣室
9A21
9A20
9A19
9A22
前室
1號電梯
2號電梯
衣間
5號電梯
6號電梯
7號電梯
訪客電梯廳
病床電梯廳
3號電梯
4號電梯
配線架室
8號電梯
9號電梯
10號電梯
輸送梯
開水/熱食間
女廁
護理師更衣室
儲藏室
9B會議室
設備器材室
工作人員用膳室
總醫師室
治療室
護理長室
9B護理站
督導室
9B05
9B03
9B02
9B01
9B21
9B20
9B19
9B22
9B醫師值班室
廁所(醫師值班室內)
9B走道
閉空間
研究大樓往北棟走廊
N4樓梯
9B06
9B07
9B08
9B09
9B10
9B11
9B12
9B13
9B15
9B16
9B17
9B18
N5樓梯
南棟往北棟走廊
外科部再生醫學及發育生物學實驗室(一)
外科部小動物手術
E4樓梯
樓梯間
電氣室
儲藏室
前室冷藏庫
骨科研究實驗室
外科部行政
走道
骨科實驗室
外科部分子生
外科部外科免疫營養實驗室
S1樓梯
9C06
9C07
9C08
9C09
9C10
9C11
9C12
9C13
9C15
9C16
9C17
9C18
S2樓梯
21號電梯
22號電梯
23號電梯
電梯廳
外科部移植及
機房
茶水間
純水設備室
研究大樓往南棟走廊
9C走道
傷口造口小組辦公室
9C護理站
9C治療室
護理長室
總醫師室
9C會議室
設備器材室
員用膳室
9C05
9C03
9C02
9C01
9C21
9C20
9C19
9C22
醫師值班室
值班室內
外科會議室
會議室
男廁
女廁
封閉空間
11號電梯
12號電梯
配線架室
15號電梯
16號電梯
17號電梯
訪客電梯廳
病床電梯廳
13號電梯
14號電梯
洗衣間
18號電梯
19號電梯
20號電梯
S3樓梯
電訊箱室
載物電梯室
電氣室
小教室
總醫師室
護理長室
9D護理站
9D檢查治療室
男護理師更衣室
9D醫師值班室
9D走道
9D05
9D03
9D02
9D01
9D19
9D18
9D17
9D20
污物室
工具室
S4樓梯
9D06
9D07
9D08
9D09
9D10
9D11
會議室/教室
9D12
9D13
9D15
9D16
S5樓梯

1 : 317