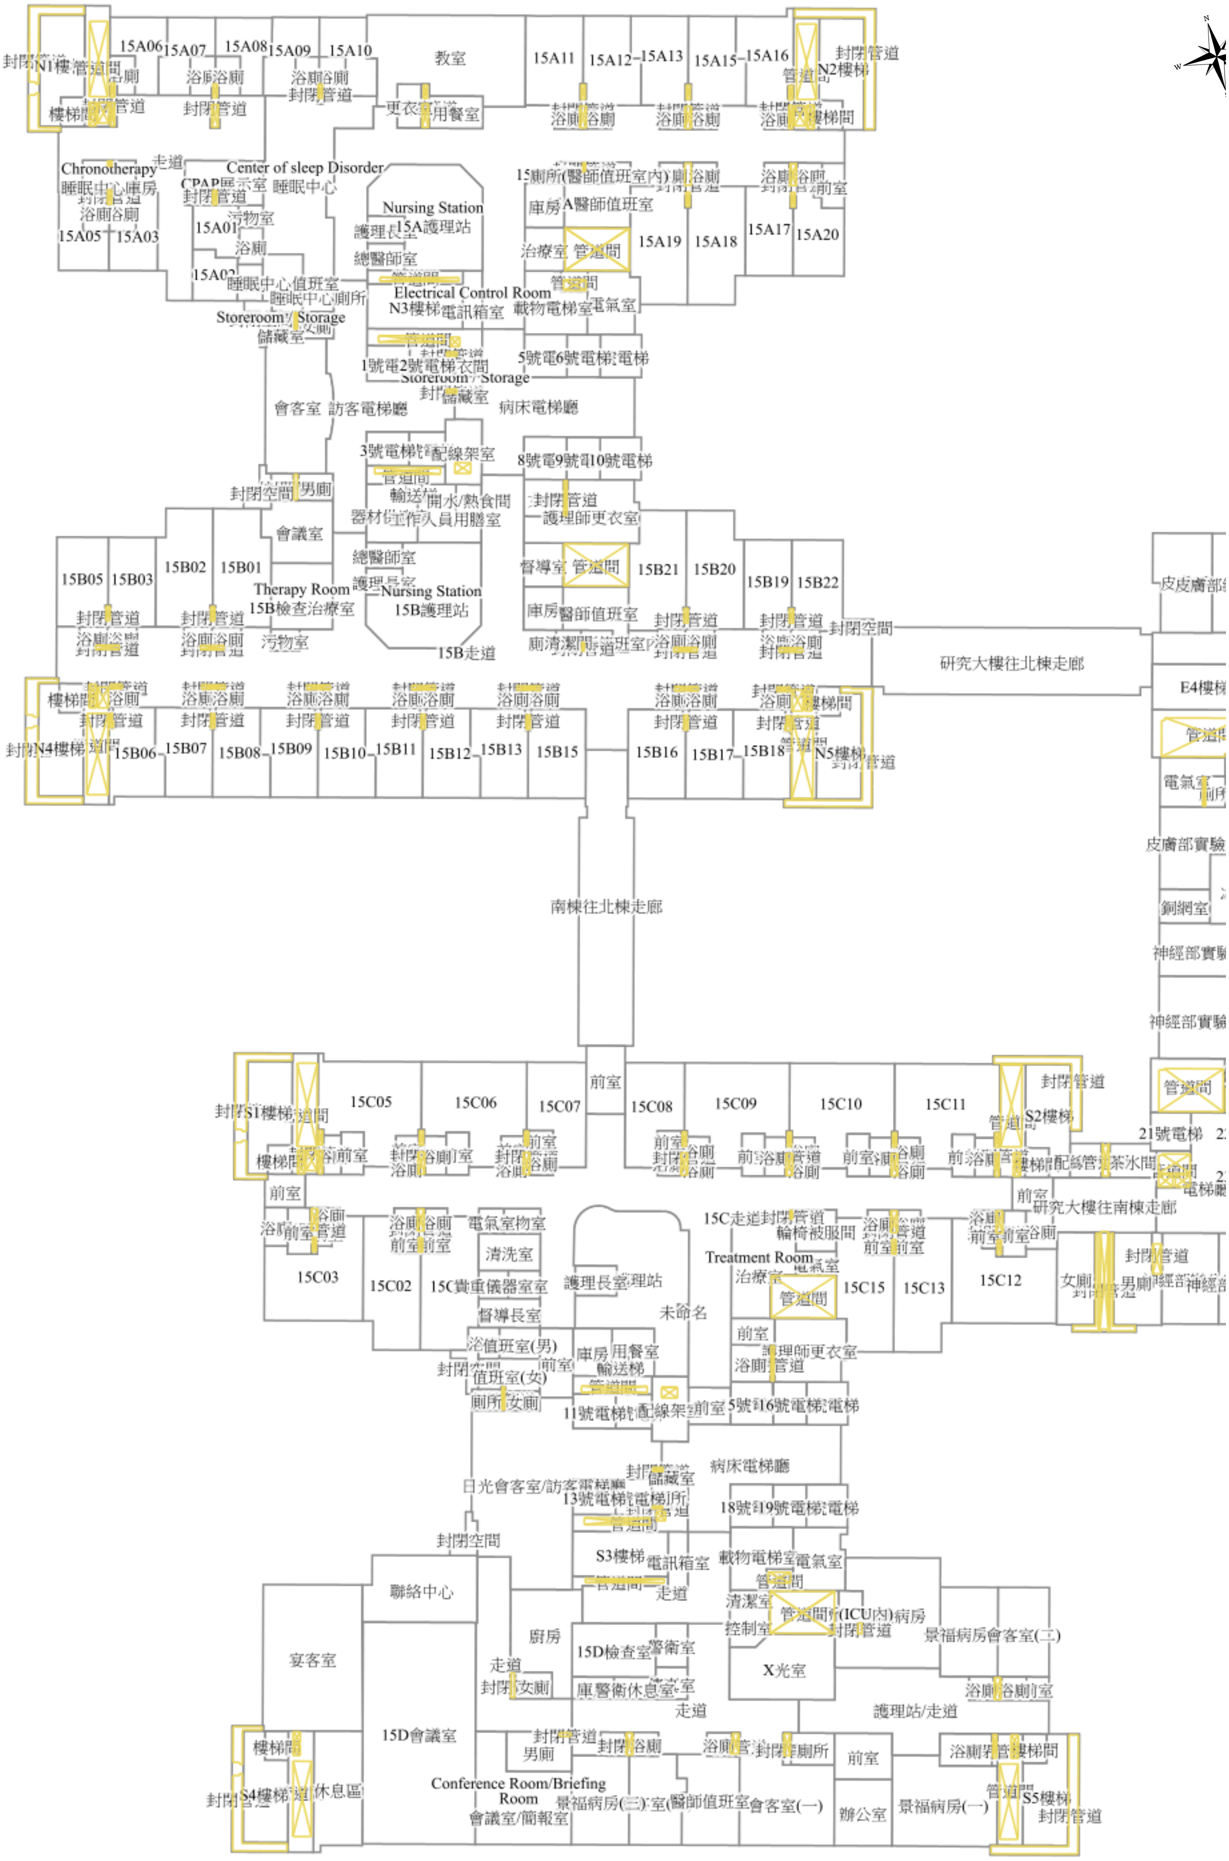
封閉管道
N1樓梯
管道間
浴廁
樓梯間
15A06
15A07
15A08
15A09
15A10
浴廁浴廁
浴廁浴廁
封閉管道
教室
更衣室
用餐室
15A11
15A12
15A13
15A15
15A16
浴廁浴廁
浴廁浴廁
浴廁
樓梯間
N2樓梯
封閉管道
Chronotherapy
睡眠中心庫房
走道
Center of sleep Disorder
CPAP展示室
睡眠中心
浴廁浴廁
15A05
15A03
15A01
污物室
浴廁
15A02
睡眠中心值班室
睡眠中心廁所
Storeroom / Storage
儲藏室
Nursing Station
護理長室
15A護理站
總醫師室
Electrical Control Room
N3樓梯
電訊箱室
載物電梯室
電氣室
廁所(醫師值班室內)
浴廁
前室
庫房
A醫師值班室
治療室
管道間
15A19
15A18
15A17
15A20
1號電梯
2號電梯
衣間
Storeroom / Storage
儲藏室
5號電梯
6號電梯
電梯
會客室
訪客電梯廳
病床電梯廳
3號電梯
配線架室
8號電梯
9號電梯
10號電梯
管道間
輸送梯
開水/熱食間
封閉管道
封閉空間
男廁
器材室
工作人員用膳室
護理師更衣室
會議室
總醫師室
15B05
15B03
15B02
15B01
Therapy Room
15B檢查治療室
護理長室
Nursing Station
15B護理站
督導室
管道間
15B21
15B20
15B19
15B22
庫房
醫師值班室
廁
清潔間
值班室
封閉管道
浴廁浴廁
污物室
15B走道
封閉空間
研究大樓往北棟走廊
樓梯間
N4樓梯
15B06
15B07
15B08
15B09
15B10
15B11
15B12
15B13
15B15
15B16
15B17
15B18
N5樓梯
封閉管道
皮膚部
E4樓梯
管道間
電氣室
廁所
皮膚部實驗
銅網室
神經部實驗
神經部實驗
南棟往北棟走廊
前室
15C05
15C06
15C07
15C08
15C09
15C10
15C11
S1樓梯
管道間
S2樓梯
封閉管道
樓梯間
前室
浴廁
21號電梯
配線管
茶水間
電梯廳
研究大樓往南棟走廊
15C03
15C02
15C貴重儀器室
電氣室
物室
清洗室
護理長室
護理站
督導長室
未命名
15C走道
輪椅被服間
Treatment Room
治療室
電氣室
15C15
15C13
15C12
女廁
男廁
神經部
值班室(男)
值班室(女)
庫房
用餐室
輸送梯
前室
護理師更衣室
廁所
女廁
11號電梯
配線架室
5號電梯
16號電梯
電梯
病床電梯廳
儲藏室
日光會客室/訪客電梯廳
13號電梯
電梯
廁所
18號電梯
19號電梯
電梯
封閉空間
S3樓梯
電訊箱室
載物電梯室
電氣室
聯絡中心
走道
清潔室
控制室
管道間
(ICU內)病房
景福病房會客室(二)
宴客室
廚房
15D檢查室
警衛室
X光室
走道
庫
警衛休息室
浴廁浴廁
護理站/走道
15D會議室
男廁
S4樓梯
休息區
Conference Room/Briefing Room
會議室/簡報室
景福病房(三)
醫師值班室
會客室(一)
前室
辦公室
景福病房(一)
S5樓梯
封閉管道

1 : 317